


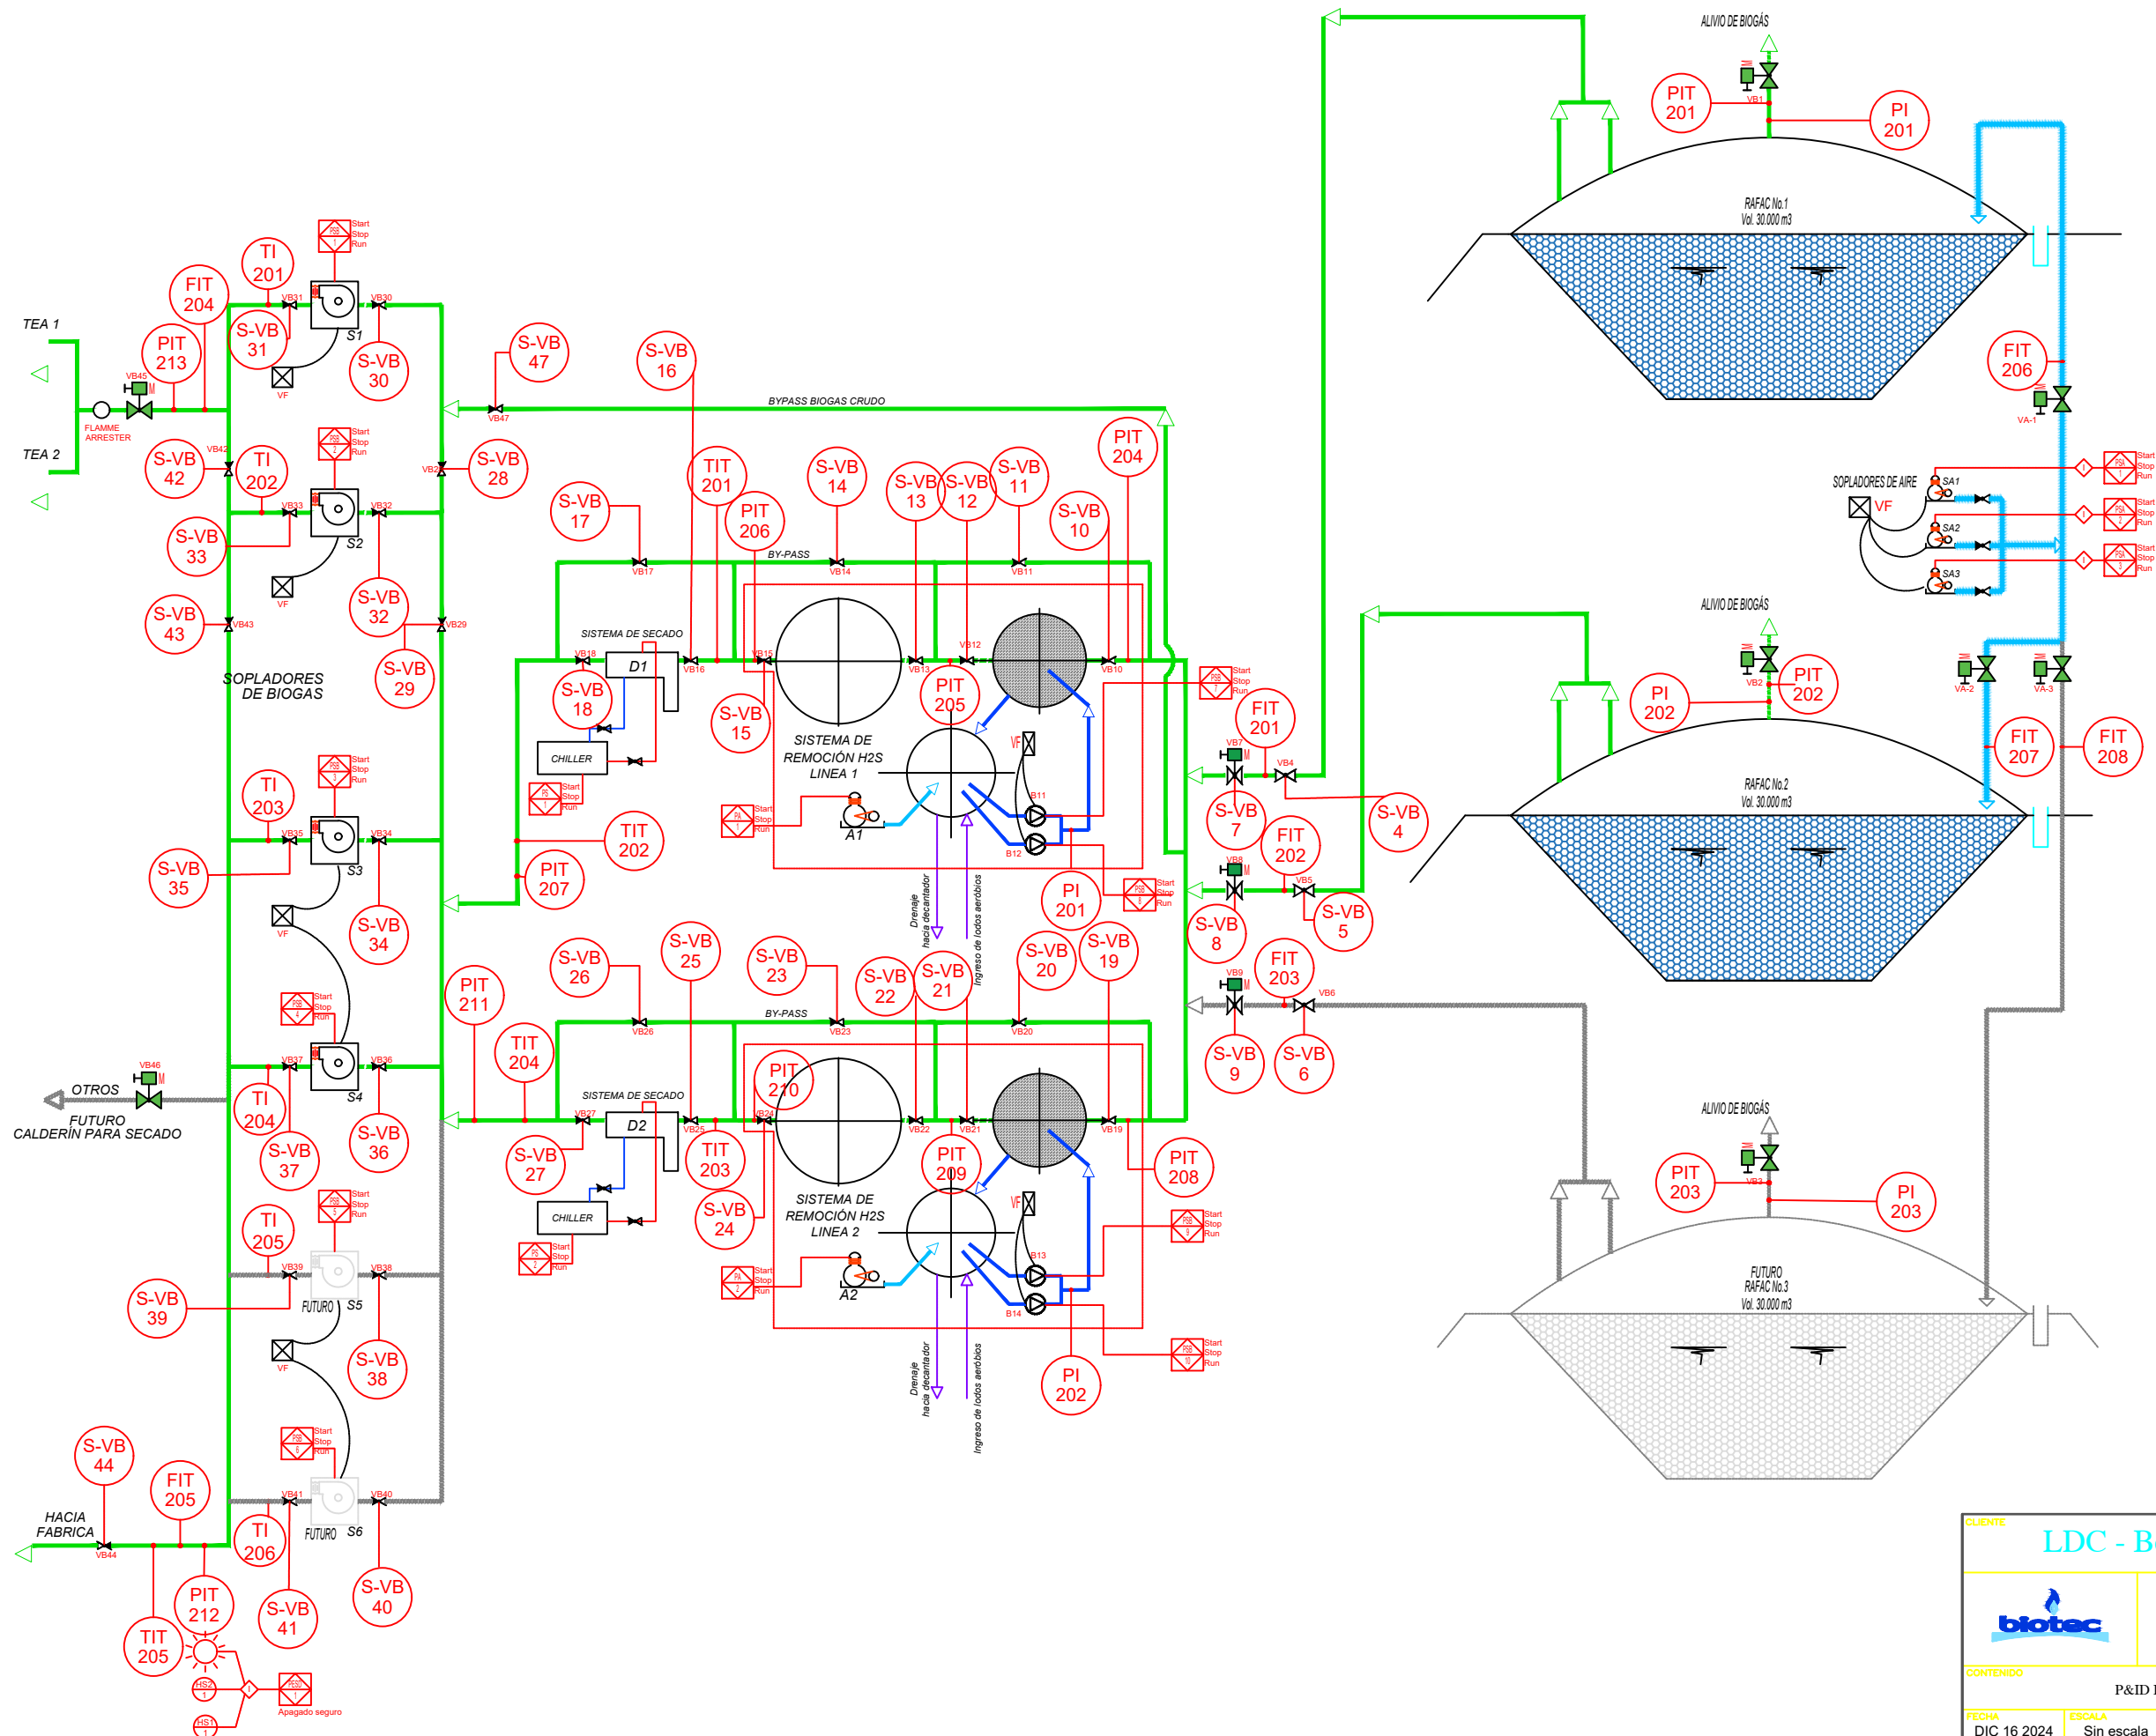

CLIENTE				
LDC - Bebedouro, Brasil				
		SISTEMA ANAEROBIO INGENERIA - ETAPA: 1		
CONTENIDO			CÓDIGO	
P&ID BIOGÁS Y AIRE			1&C02	
FECHA	ESCALA	DISEÑO:	REVISIÓN	CONSECUTIVO
DIC 16 2024	Sin escala	AA-JCB	PV	PJ 24-73
Propiedad intelectual de BIOTEC INTERNATIONAL - Se prohíbe su copia o divulgación				