


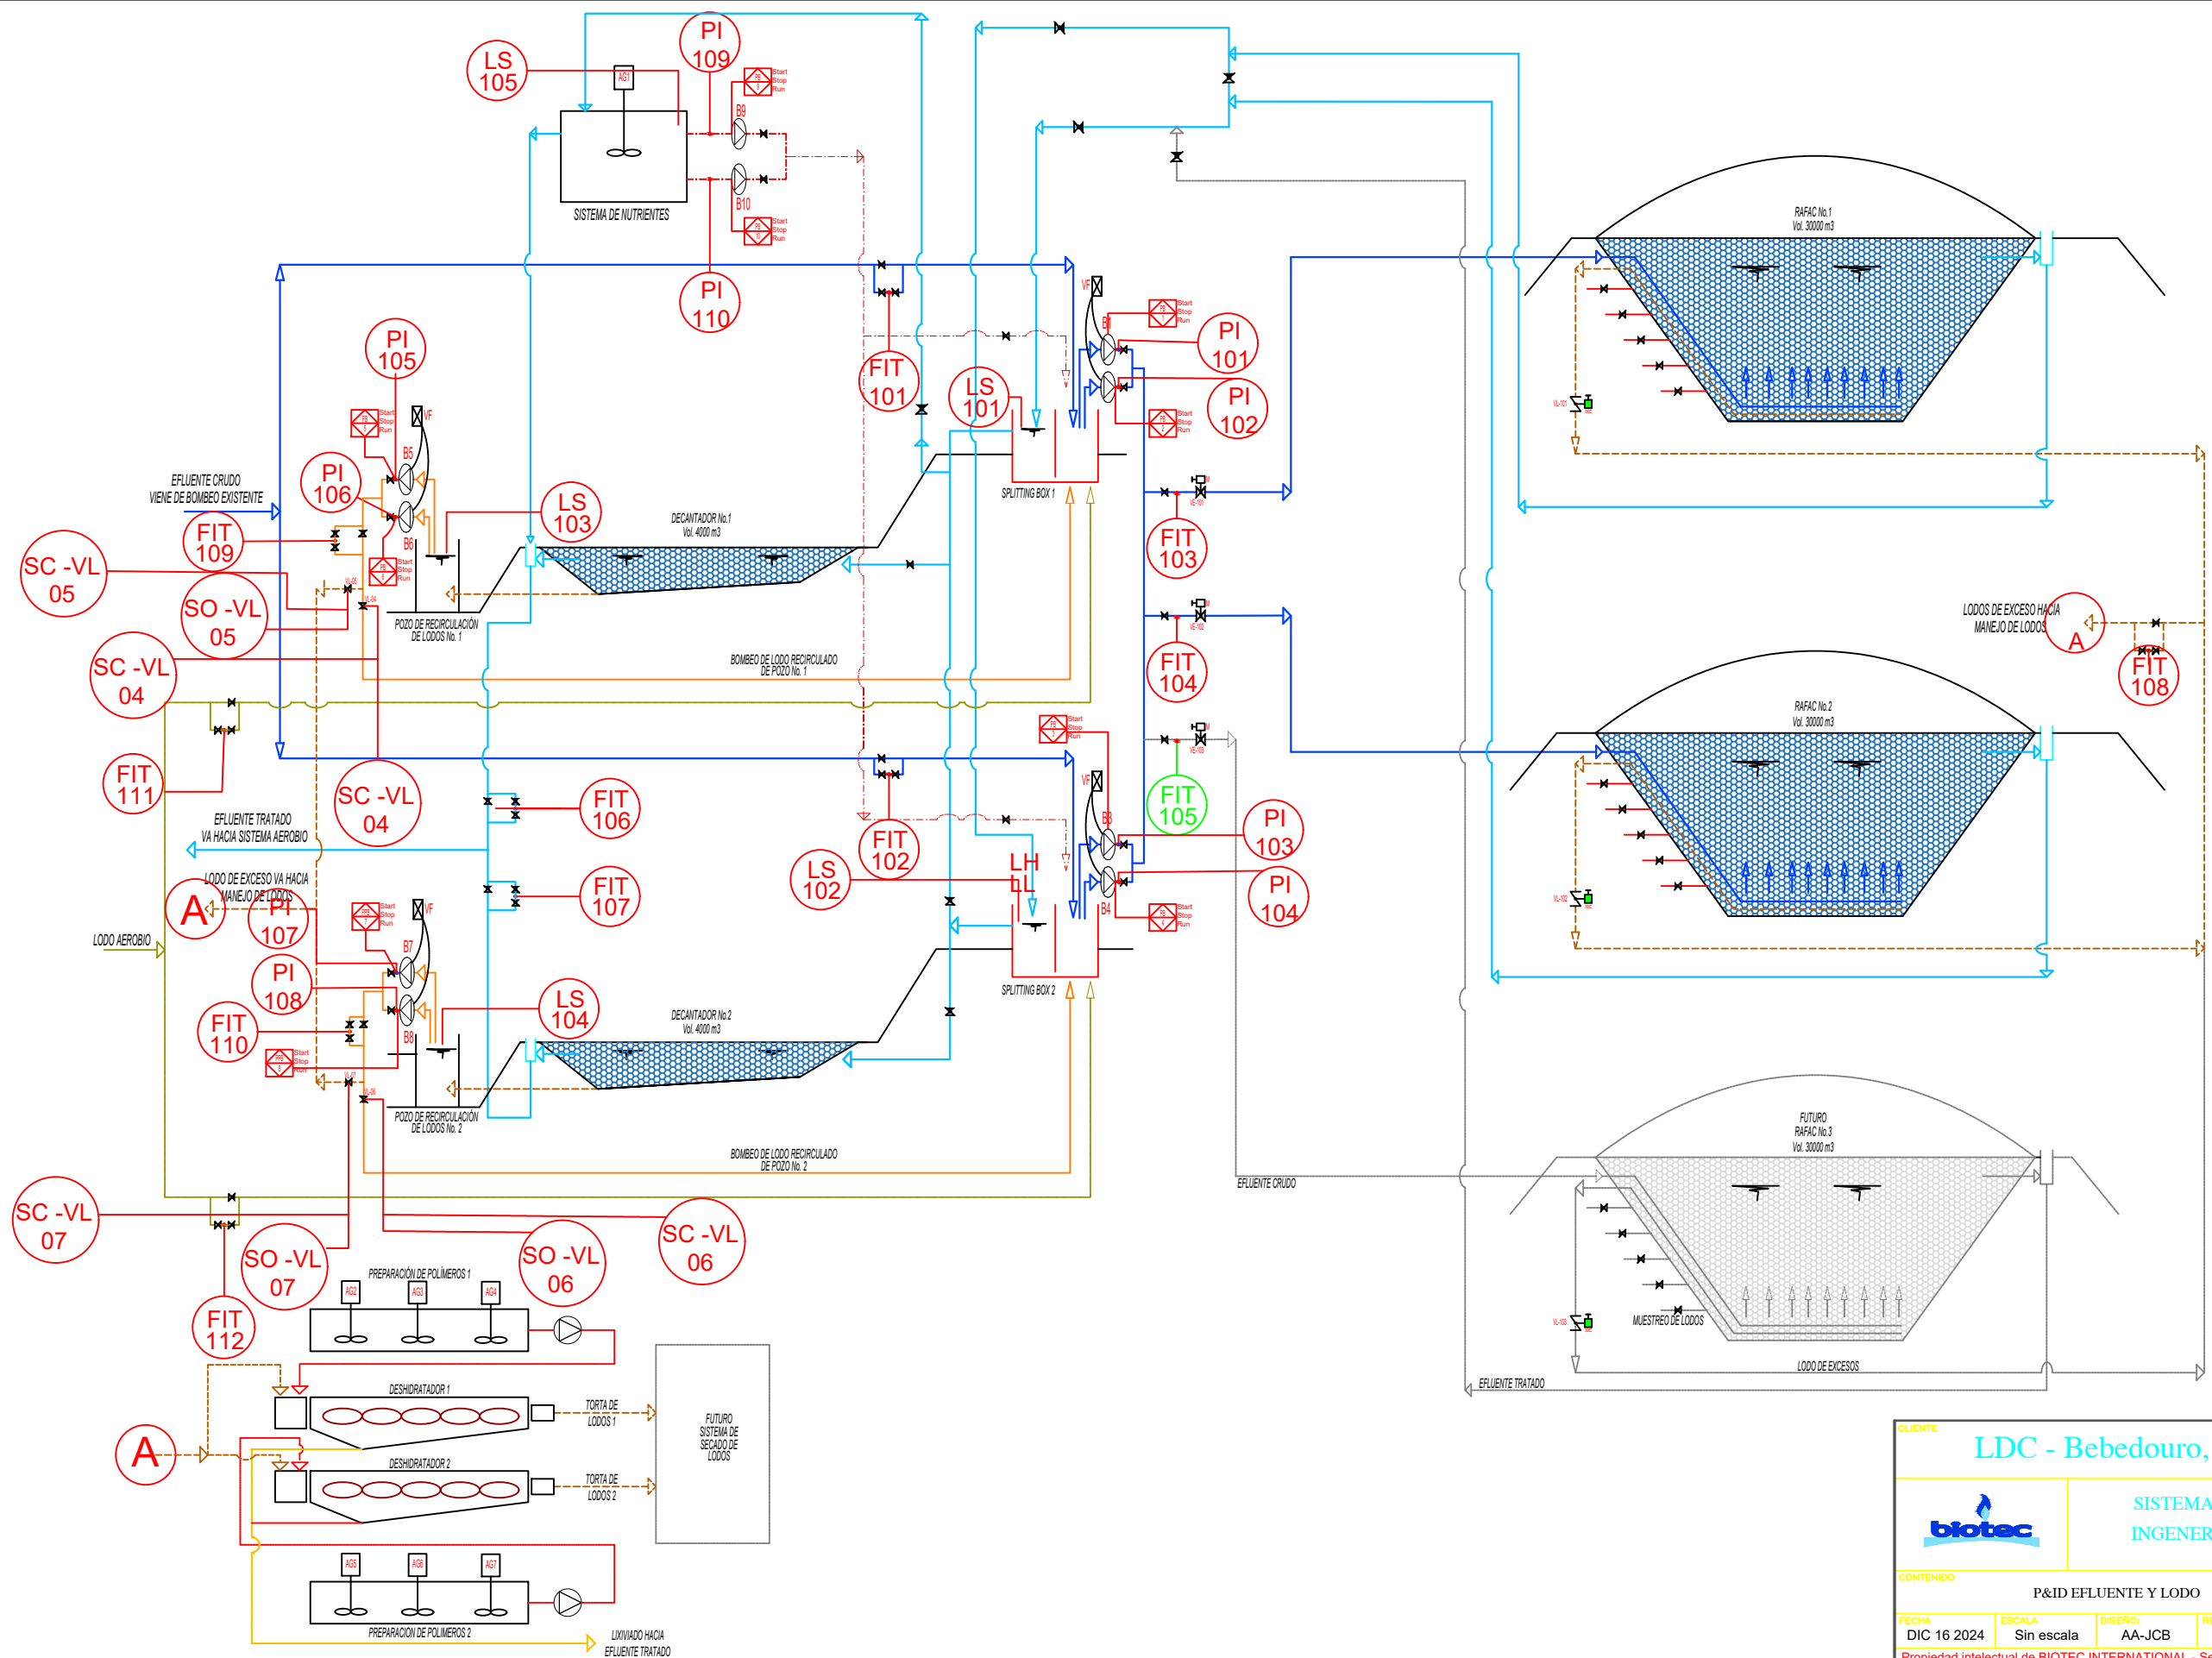

CLIENTE				
LDC - Bebedouro, Brasil				
		SISTEMA ANAEROBIO INGENERIA - ETAPA: 1		
CONTENIDO				CÓDIGO
P&ID EFLUENTE Y LODO				I&C01
FECHA	ESCALA	DISEÑO	REVISIÓN	CONSECUTIVO
DIC 16 2024	Sin escala	AA-JCB	PV	PJ 24-72
Propiedad intelectual de BIOTEC INTERNATIONAL - Se prohíbe su copia o divulgación				