


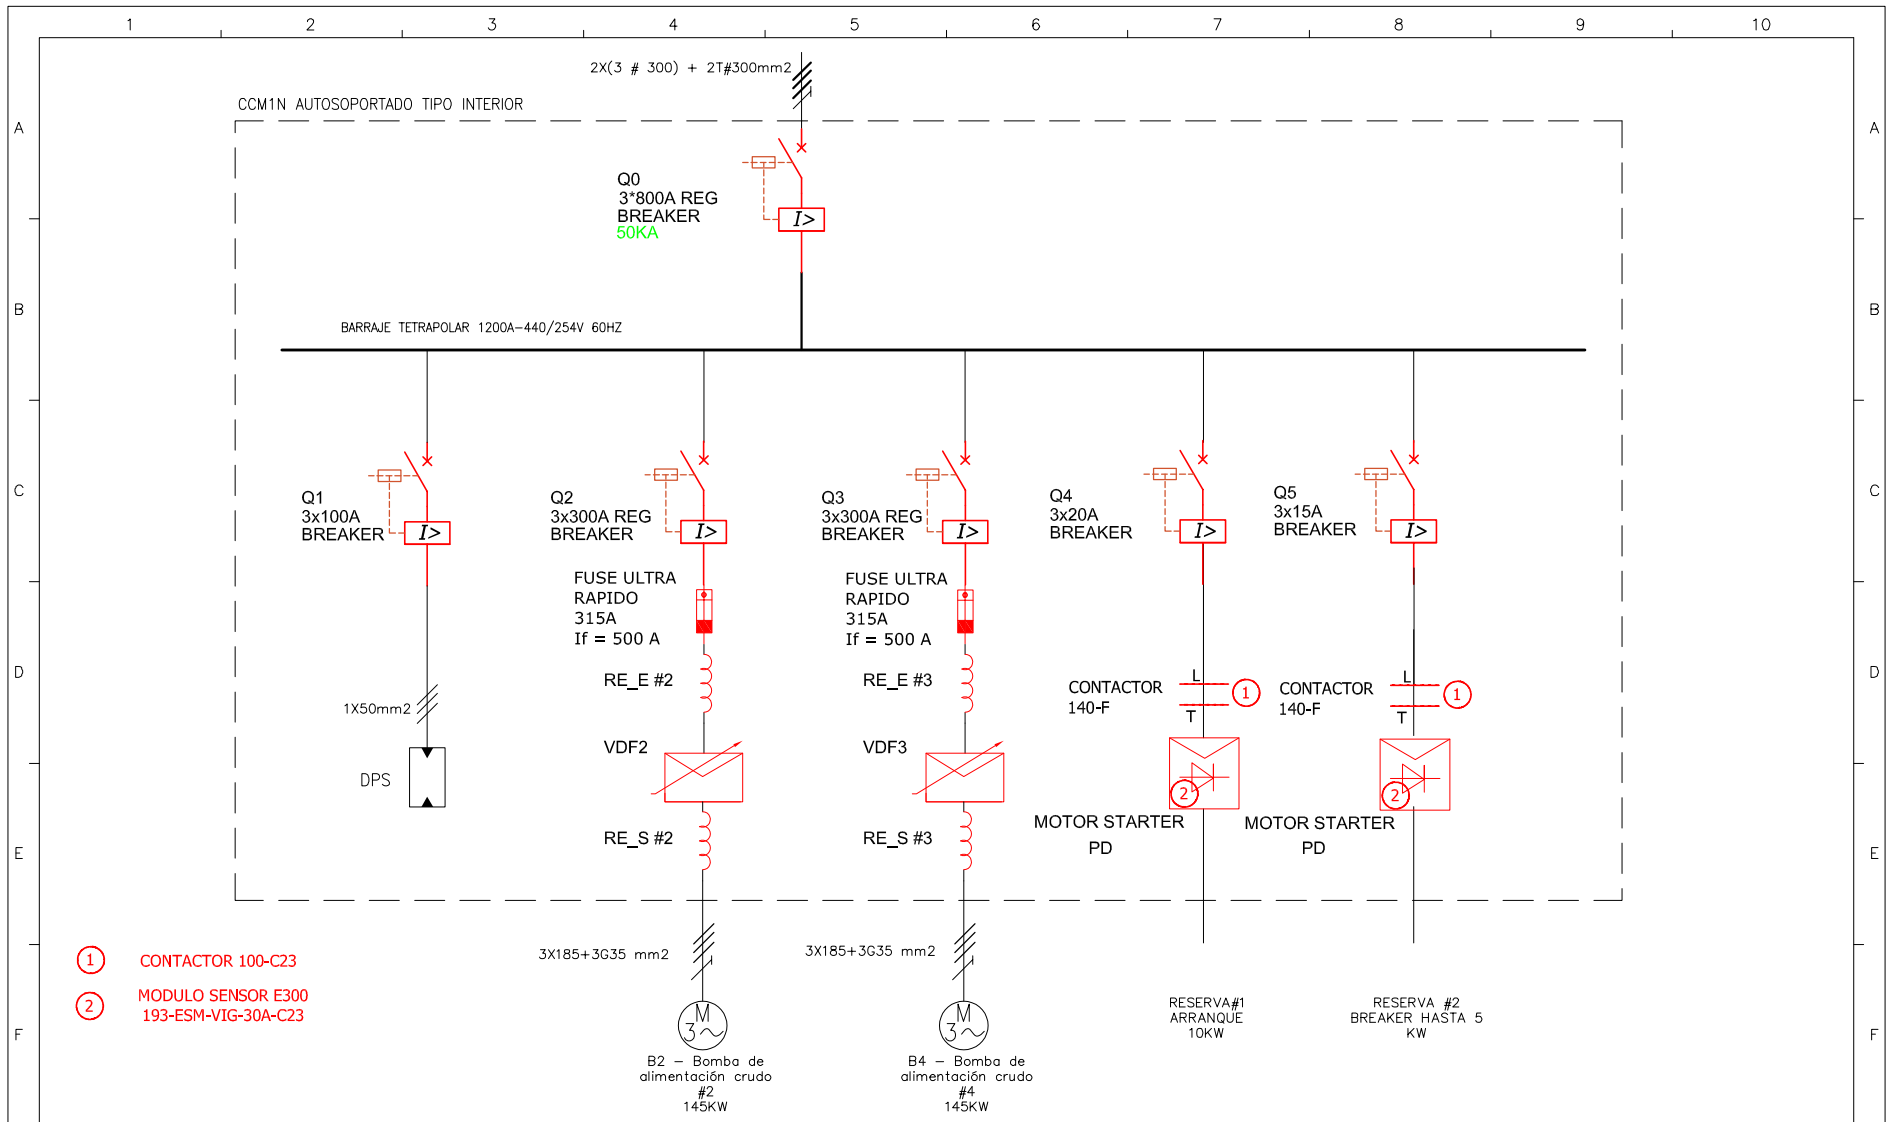

CLIENTE:
LDC

PROYECTO:
PLANTA DE GAS LDC

DESCRIPCIÓN:
DIAGRAMA UNIFILAR CCM1 N

APROBO:
PAULO VALENCIA

REVISO:
ALBERTO ARIAS

DIBUJO:
STEVEN VARELA

REVISIONES				
REV	REVISADO	APROBO	FECHA	DESCRIPCION
V0	A. ARIAS	P. V.	10/09/2024	VERSIÓN FINAL

CAPITULO: TABLERO CCM1 N		
NOMBRE DOC: ELE_01_CCM1N_02		
FECHA: SEPT 10	PAGINA: 2	DE: 2

No CONTRATO:
No_CONTRATO